
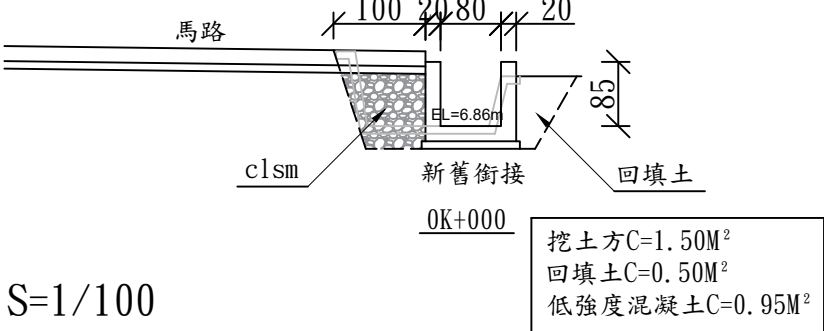
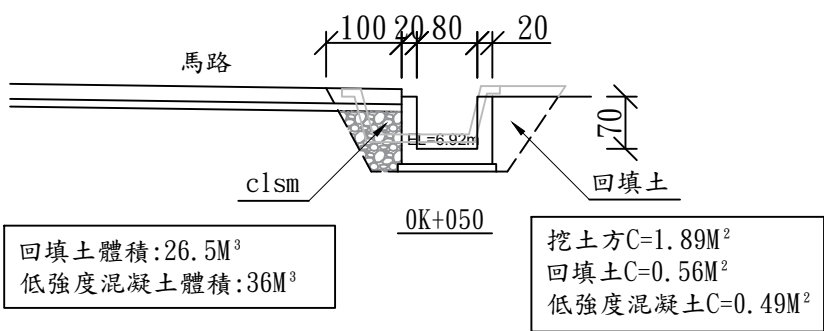
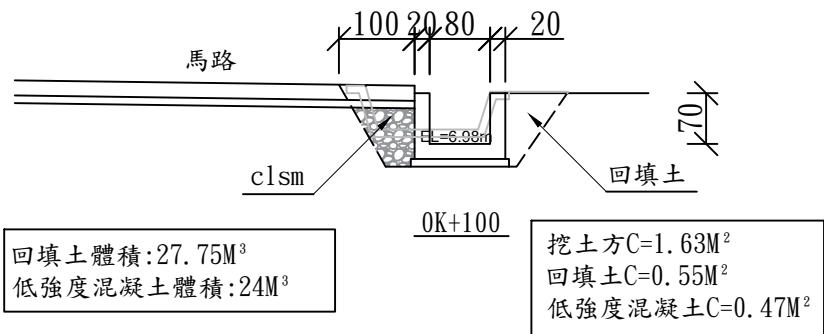
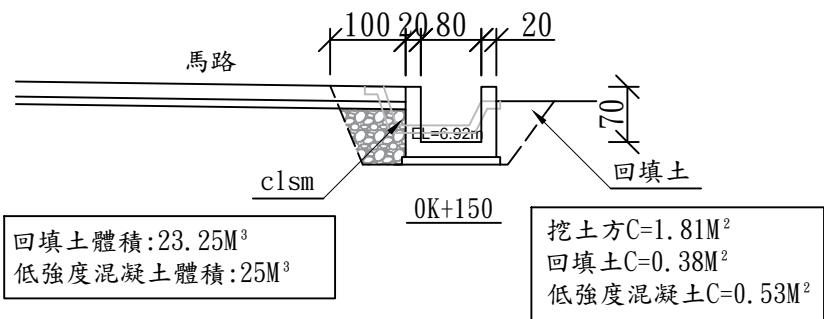







回填土體積合計:263.75M³
低強度混凝土體積合計:94.54M³

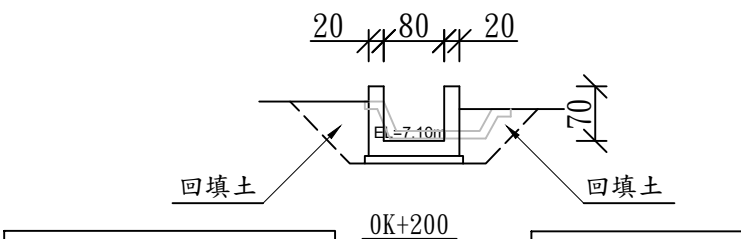


S=1/100

混凝土規定需求：

- 1.除另有規定者外，水泥採用卜特蘭第1型水泥，並符合中國國家標準CNS 61 R2001。
- 2.混凝土粒料須符合CNS 1240 A2029規範標準。水泥含量須達[75%]。
- 3.未經業主及監造人認可之混凝土不得進入工地。

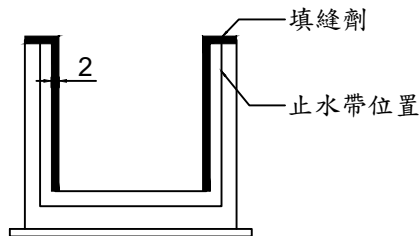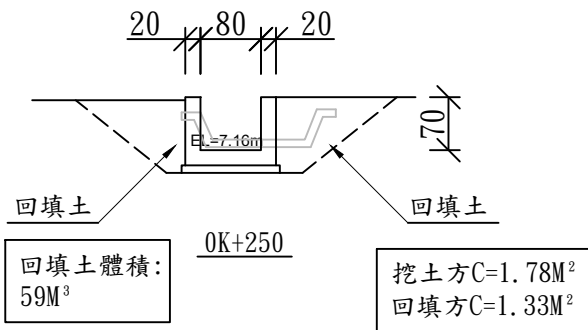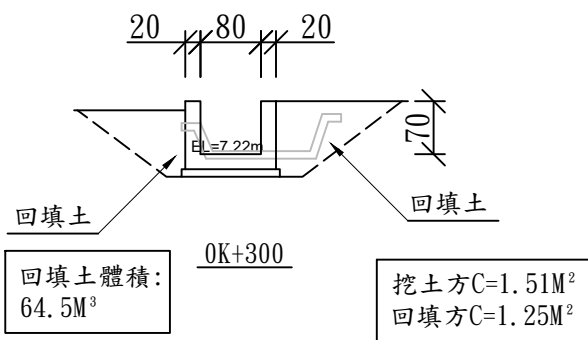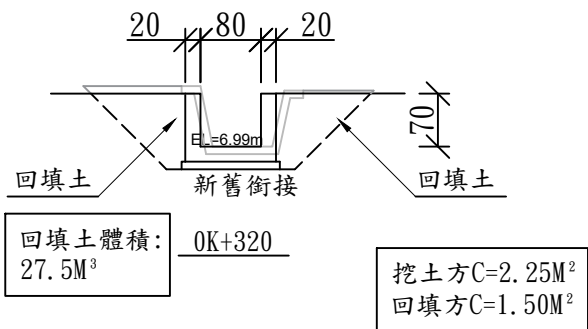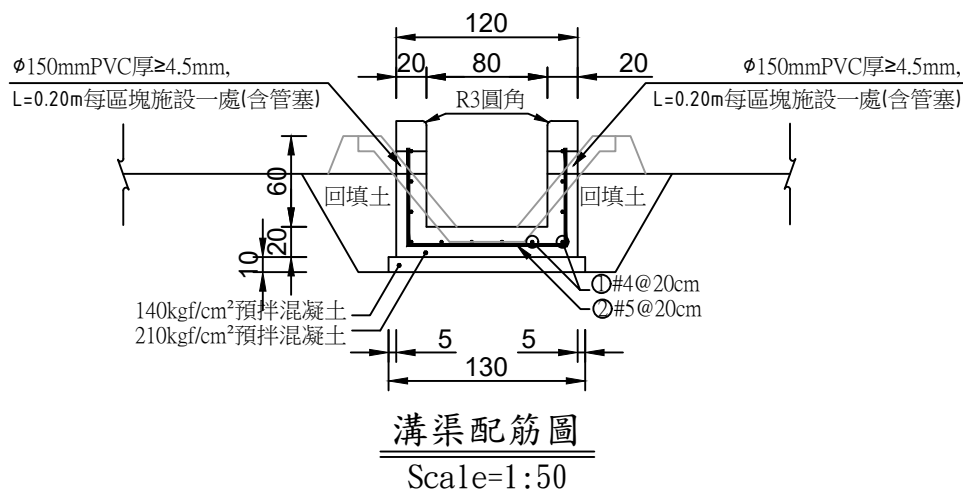

PVC止水帶斷面圖
Scale=N. T. S.

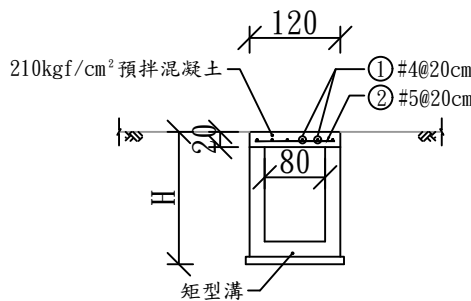

水泥板橋標準斷面圖
Scale=1:100

填縫膠品質要求表

項 目	要 求
比重	標示值±0.10
硬度(Hs)	10~30
抗拉強度 kPa { kgf/cm ² }	1178{ 12 }以上
伸長率(%)	600 以上
撕裂強度 N/cm { kgf/cm }	58.8{ 6 }以上
下垂度(mm)	0
老化試驗	硬度(Hs) 10~30 抗拉強度保留率(%) 80 以上 伸長率保留率(%) 80 以上 撕裂強度保留率(%) 80 以上


伸縮縫填縫膠材料說明

1. 填縫膠採用聚脲酯類材料，須符合CNS 6985 A2090之規定。

伸縮縫填縫板材料說明

1. 填縫板材料得採用：

- (1) 保麗龍
 - (2) 夾板
 - (3) 保麗龍外覆夾板材料
2. 填縫板材料應為一體成型，不得採拼接方式。

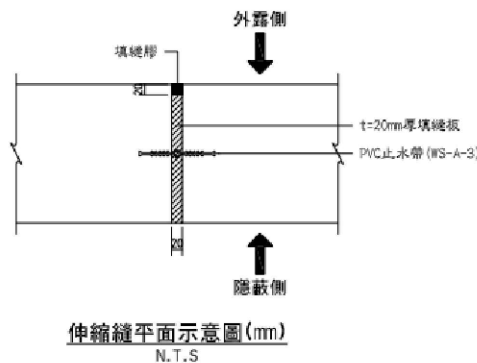


伸縮縫平面示意圖(mm)
N.T.S

PVC止水帶規格：

種類	標稱尺寸 (MM)	寬度 B (MM)	厚度 T (MM)	H (MM)	D (MM)	鍵數	參考重量 (KG/M)
WS-A-3	220X9	220±50	9,0±0,9	15	18±2	10以上	2.8

註：結構厚度>0.20m，PVC止水帶採用WS-A-3型或依設計圖之指示。

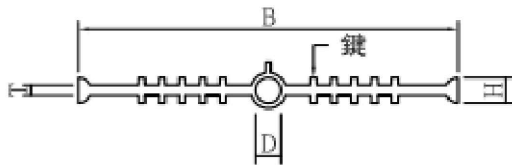

PVC止水帶示意圖
Scale=N. T. S.

1. 既有水泥板橋出入口 L=5.0M*7座=35M
2. 與既有出入口需銜接平順，相關費用已計入構造物銜接費用內

水泥板橋 數量表 單位:cm								
型狀尺寸		鋼筋 稱號	間距 (cm)	長度 (cm)	支/M	總長度 (m)	單位重 (kg/m)	總重 (kg)
1	100	#4	20.0	100	6	6.00	0.994	5.96
2	105	#5	20.0	105	5	5.25	1.560	8.19
鋼筋數量		#4	5.96		SD280=14.15KG			
		#5	8.19					
210kg/cm ² 預拌混凝土(m ³)			0.8*0.2*1					0.16m ³
模板(m ²)			0.2*2+0.8					1.20m ²

版次 VER	日期 DATE	修正者 REV. BY	修正 DESCRIPTION	主 辦 機 關 雲 林 縣 政 府	設 計 單 位 誼固工程顧問有限公司		比例尺 SCALE 如圖示	技師簽證	褒忠鄉東馬鳴山農地重劃區六勝段196地號給水溝改善工程		
					繪圖 DRAWIN 李冠杰	複審 RECHECKED 郭敬泓	單位 UNIT CM		橫斷面圖		
					審圖 CHECKED 郭敬泓						
									圖號 DRG. NO. A04		
									張數 06/08		